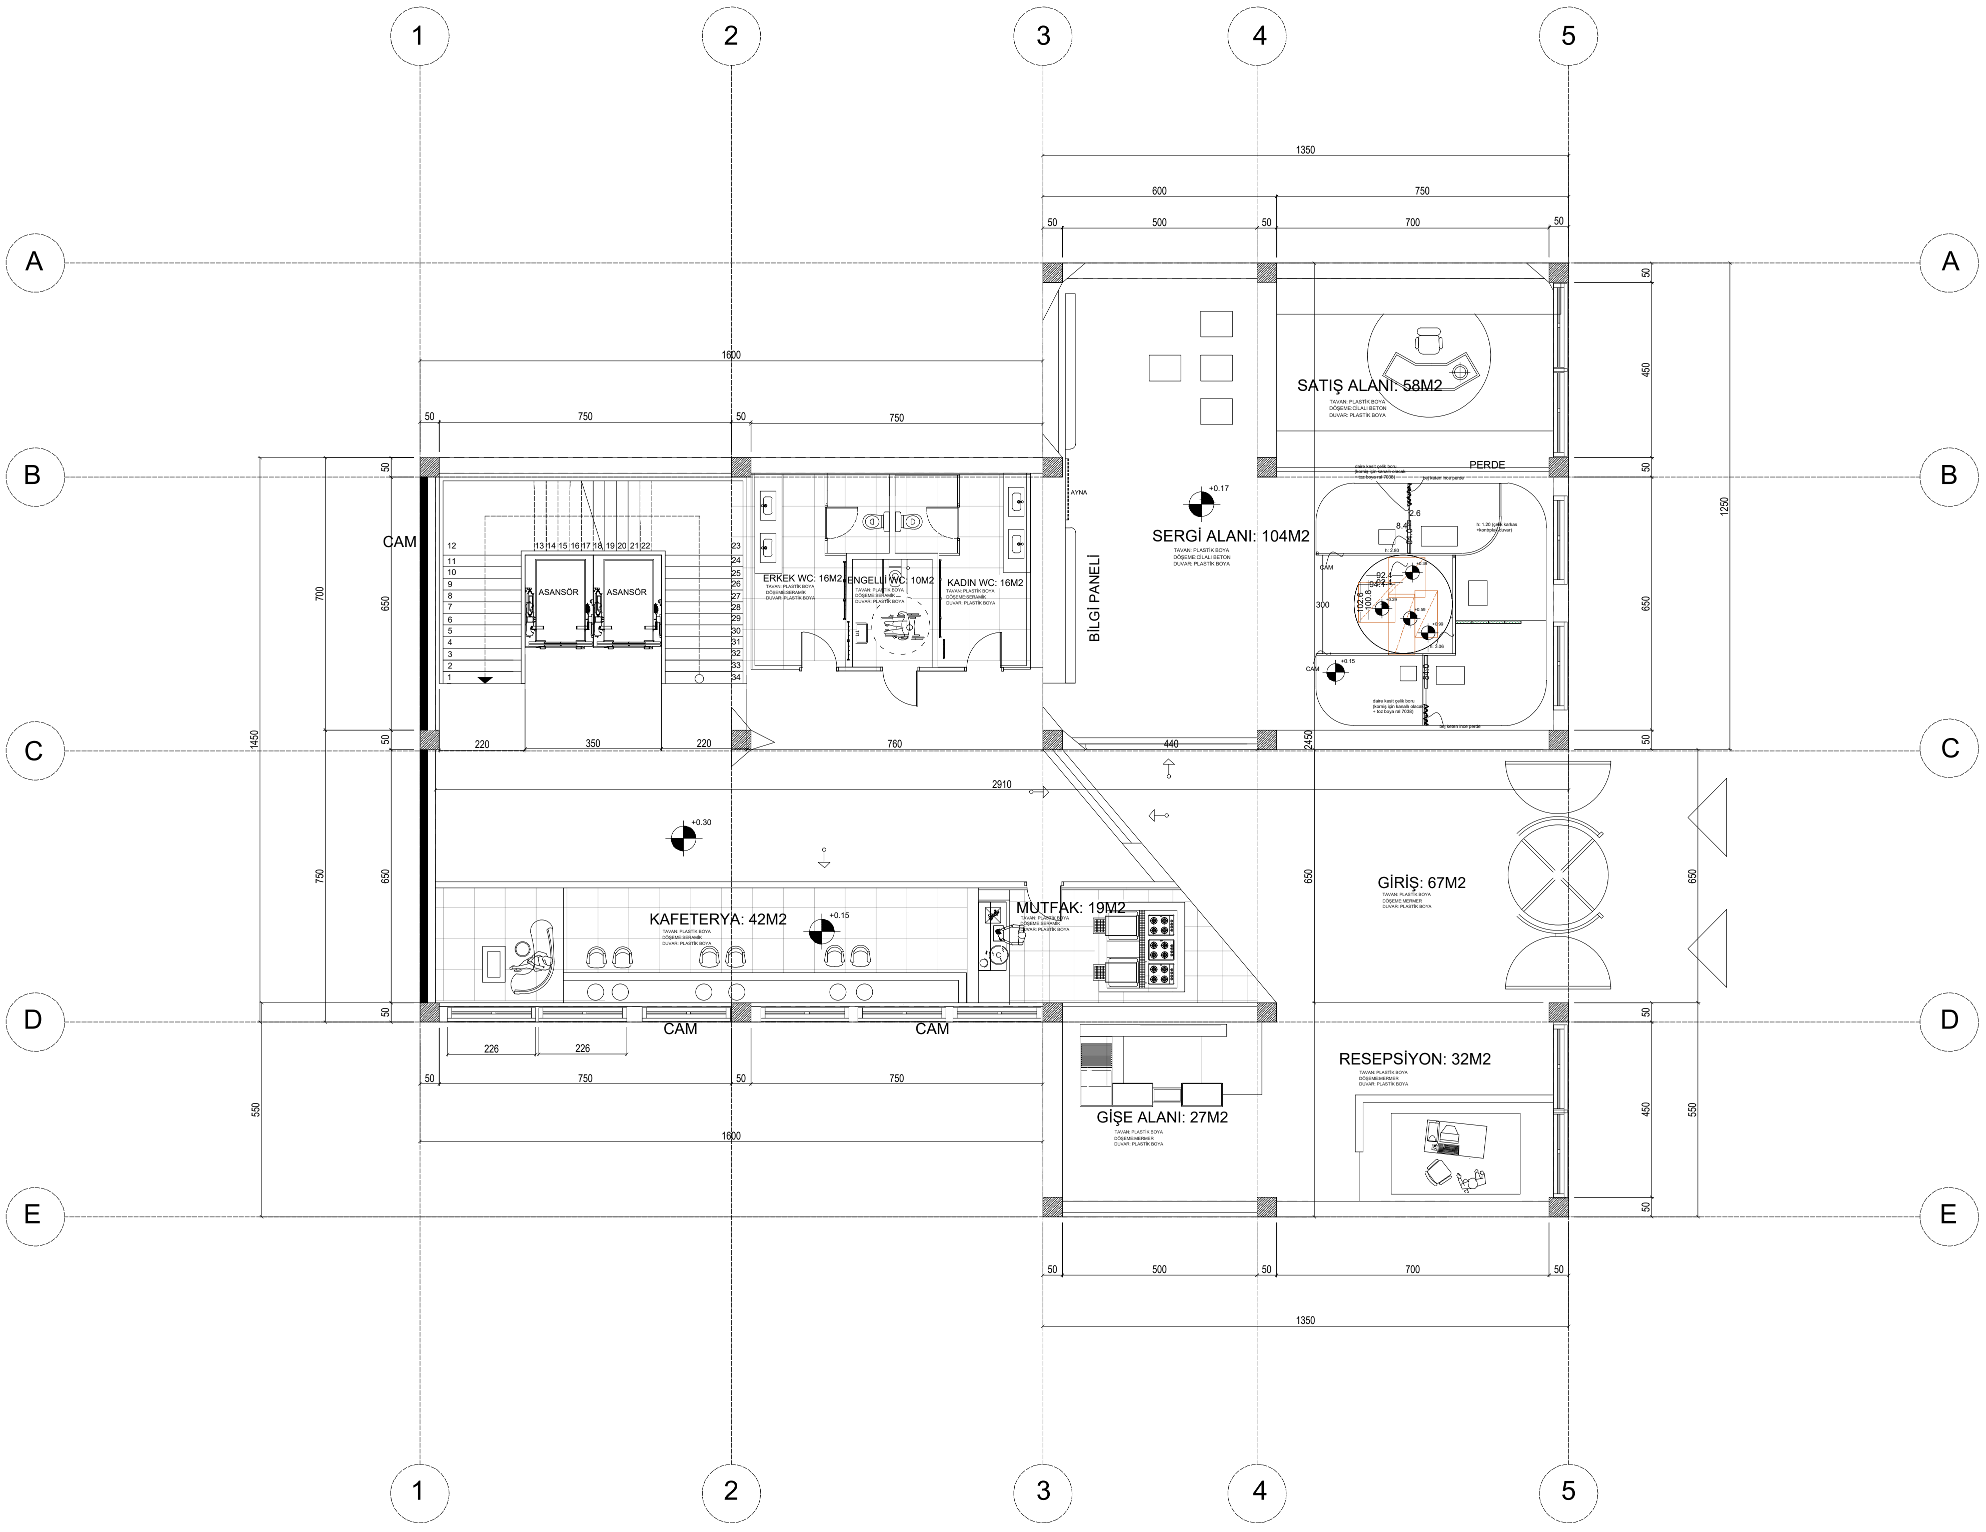
1
2
3
4
5
A
B
C
D
E
1350
600
750
50
500
50
700
50
1600
50
750
50
750
CAM
12
11
10
9
8
7
6
5
4
3
2
1
13 14 15 16 17 18 19 20 21 22
23
24
25
26
27
28
29
30
31
32
33
34
ASANSÖR
ASANSÖR
ERKEK WC: 16M2
TAVAN: PLASTİK BOYA
DÖŞEME:SERAMİK
DUVAR: PLASTİK BOYA
ENGELLİ WC: 10M2
TAVAN: PLASTİK BOYA
DÖŞEME:SERAMİK
DUVAR: PLASTİK BOYA
KADIN WC: 16M2
TAVAN: PLASTİK BOYA
DÖŞEME:SERAMİK
DUVAR: PLASTİK BOYA
AYNA
BİLGİ PANELİ
+0.17
SERGİ ALANI: 104M2
TAVAN: PLASTİK BOYA
DÖŞEME:CİLALI BETON
DUVAR: PLASTİK BOYA
SATIŞ ALANI: 58M2
TAVAN: PLASTİK BOYA
DÖŞEME:CİLALI BETON
DUVAR: PLASTİK BOYA
PERDE
daire kesit çelik boru
(korniş için kanallı olacak
+ toz boya ral 7038)
bej keten ince perde
2.6
8.4
h: 2.80
h: 1.20 (çelik karkas
+kontrplak duvar)
CAM
300
92.4
92.4
94.1
102.6
100.8
+0.39
+0.29
+0.59
+0.99
h: 3.06
CAM
+0.15
daire kesit çelik boru
(korniş için kanallı olacak
+ toz boya ral 7038)
bej keten ince perde
50
700
650
50
1450
220
350
220
760
440
2450
1250
2910
+0.30
650
750
650
KAFETERYA: 42M2
TAVAN: PLASTİK BOYA
DÖŞEME:SERAMİK
DUVAR: PLASTİK BOYA
+0.15
MUTFAK: 19M2
TAVAN: PLASTİK BOYA
DÖŞEME:SERAMİK
DUVAR: PLASTİK BOYA
GİRİŞ: 67M2
TAVAN: PLASTİK BOYA
DÖŞEME:MERMER
DUVAR: PLASTİK BOYA
650
50
CAM
CAM
226
226
50
750
50
750
1600
550
GİŞE ALANI: 27M2
TAVAN: PLASTİK BOYA
DÖŞEME:MERMER
DUVAR: PLASTİK BOYA
RESEPSİYON: 32M2
TAVAN: PLASTİK BOYA
DÖŞEME:MERMER
DUVAR: PLASTİK BOYA
450
550
50
50
500
50
700
50
1350